


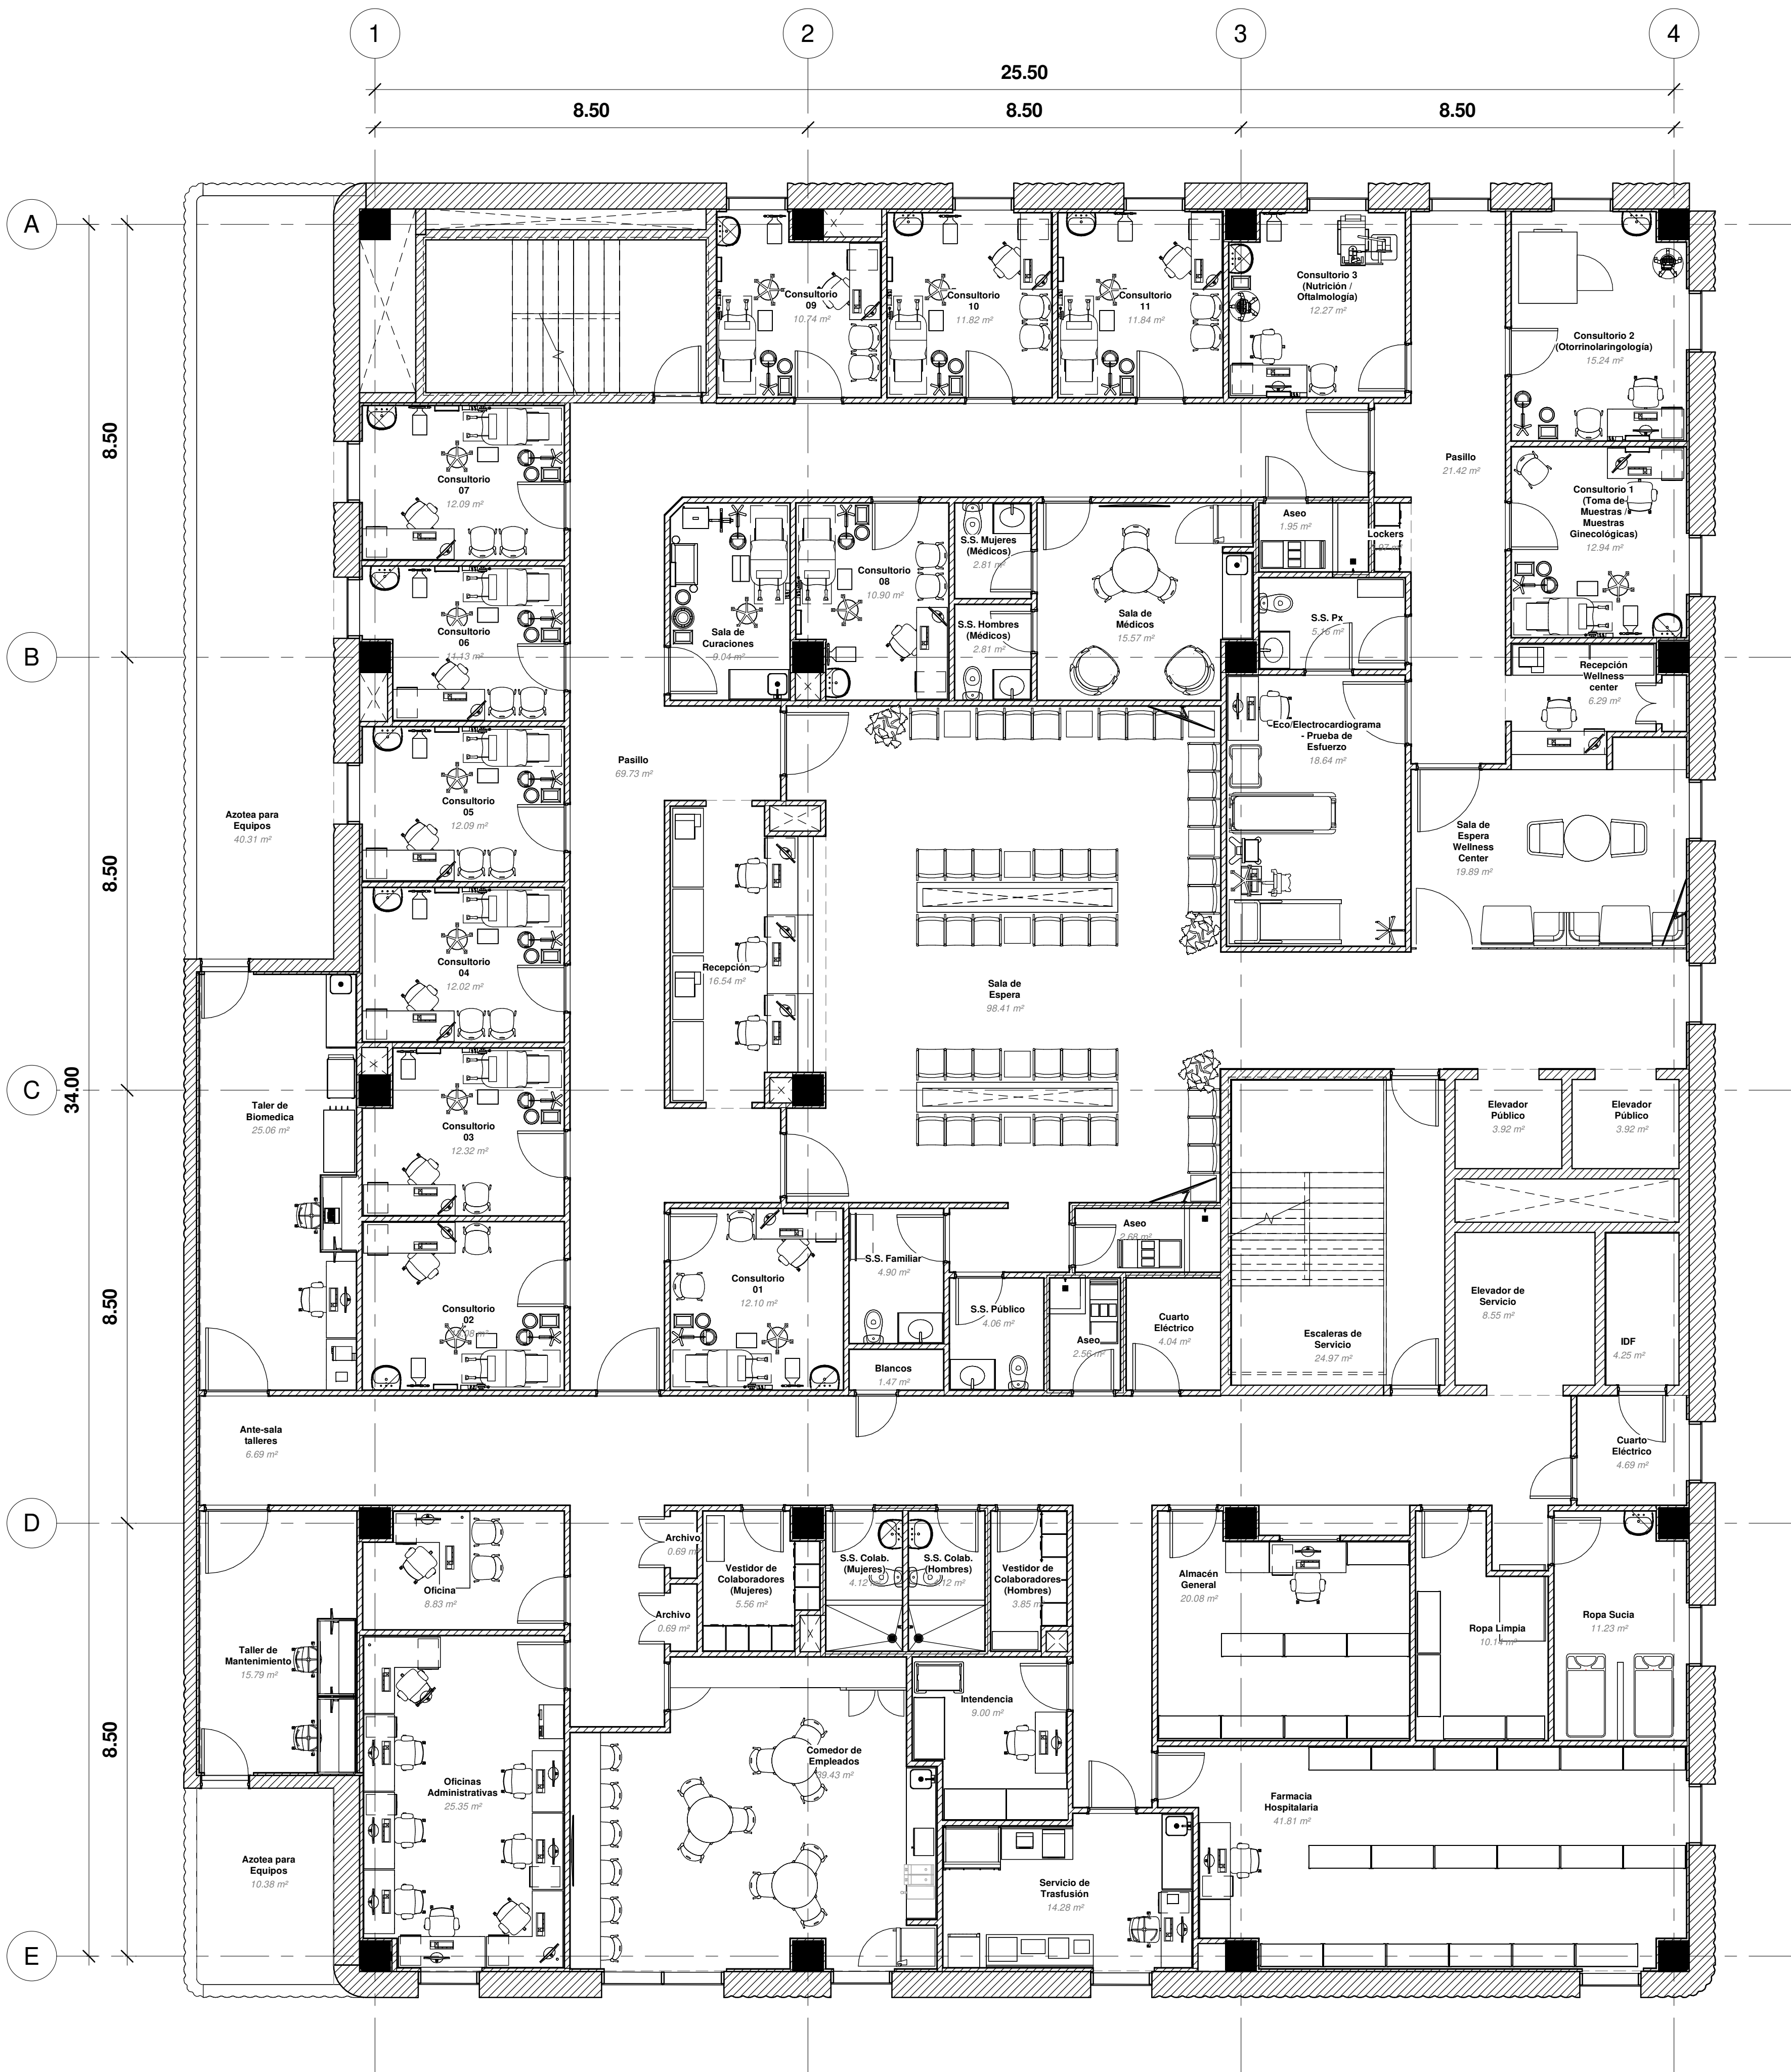

0.01-DD-2N - Segundo Nivel - Planta Arquitectónica

Escala 1 : 75

NOTAS:

Los planos presentados en esta entrega forman parte de la etapa de Desarrollo de Diseño, por lo que todos estos planos están sujetos a cambios y actualizaciones futuras, las cuales se verán reflejadas formalmente en la entrega de la etapa de Documentos Constructivos. Por lo tanto este material NO debe ser utilizado para construcción.

BITÁCORA DE CAMBIOS		
ÁREA	DESCRIPCIÓN	FECHA:
AZOTEA PARA EQUIPOS	SE TOMA ESPACIO DE AZOTEA PARA UBICAR TALLERES DE MANTENIMIENTO Y BIOMÉDICA.	01 DE JULIO DE 2026
CUARTO ELÉCTRICO	SE UBICA CUARTO ELÉCTRICO FRENTE A IDF	01 DE JULIO DE 2026
CONSULTORIOS 2 Y 3	SE PRESCINDE DE LOS SANITARIOS DE LOS CONSULTORIOS PARA GENERAR PASILLO HACIA AZOTEA	01 DE JULIO DE 2026

01 de Julio de 2026
PLANO PRELIMINAR
PLANO DE
DESARROLLO DE DISEÑO
Versión 2
Taller de Diseño
Arquitectónico



DAGP | PLANEACIÓN Y DISEÑO DE PROYECTOS

PROYECTO: CMSA05 - CCA Saltillo
CODIGO: 0.01-DD-2N DIBUJÓ: KAGM
REVISIÓN: V-02 FECHA: 01 de Julio de 2026
ESCALA: 1 : 75
UNIDAD DE SERVICIO: CM Parque Centro