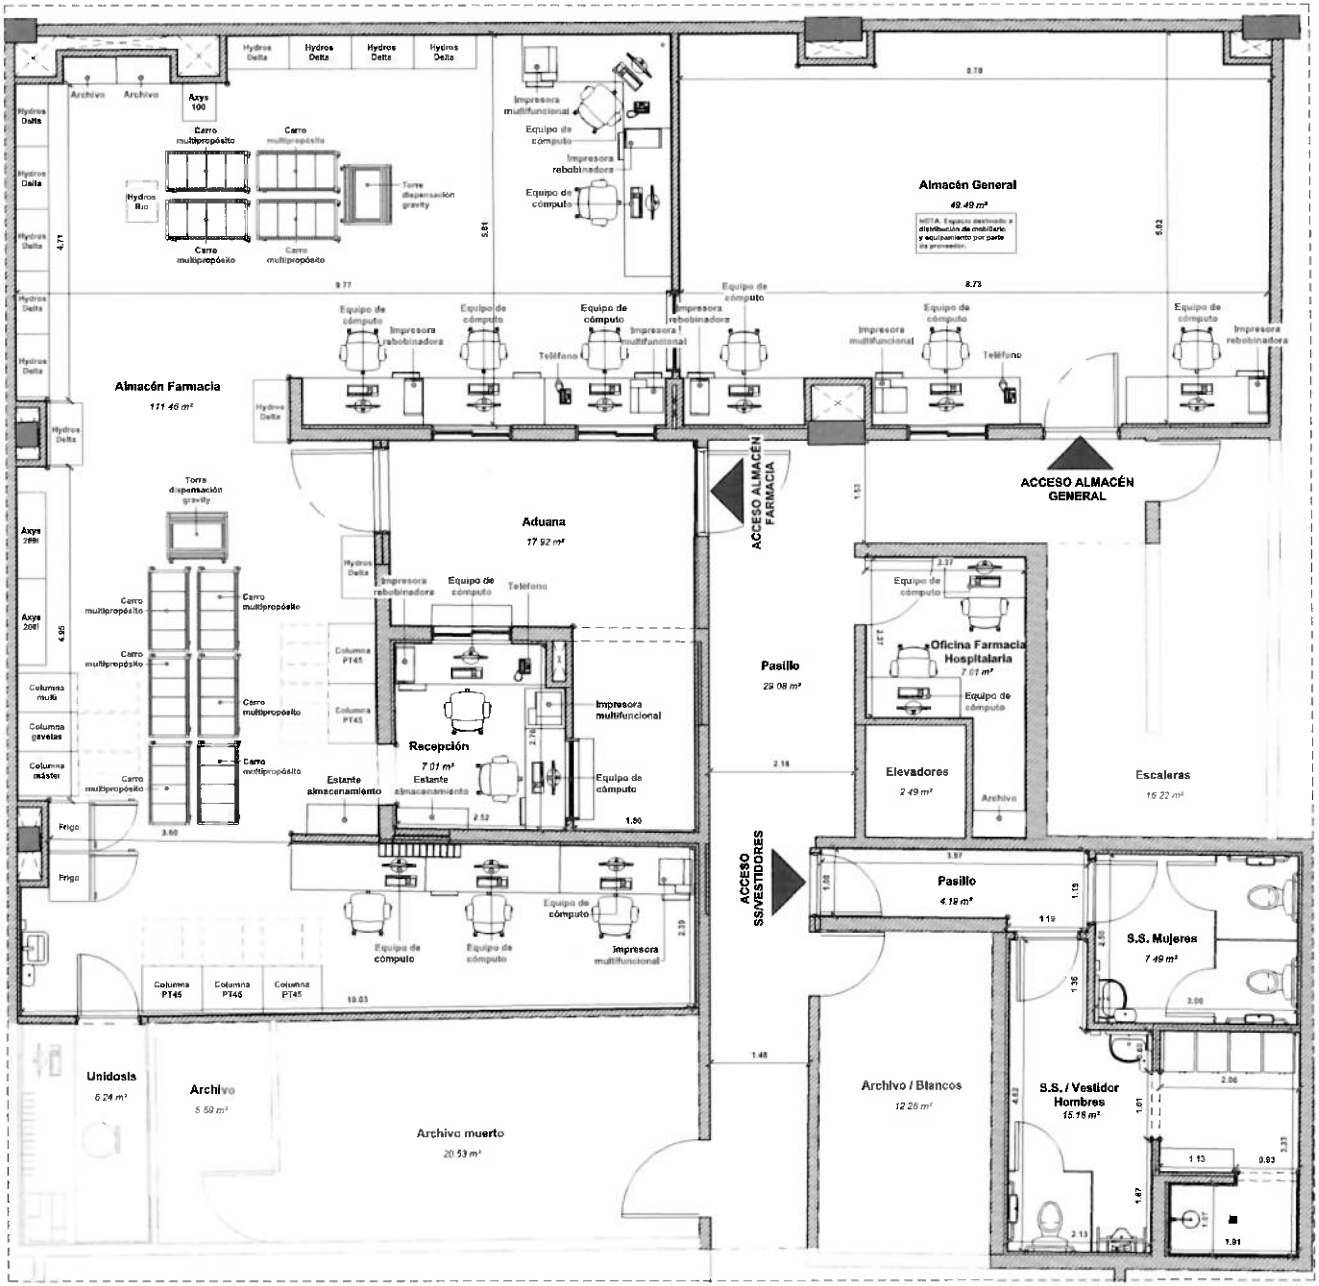


CMV84-V01-ARQ-01 - Planta Arquitectónica

1 : 50

22/05/26

22/05/26

CHRISTUS MUGUERZA
Sistema de Salud

22 de Mayo de 2026
Documentos constructivos
PLANO AUTORIZADO PARA CUANTIFICACIÓN
Taller de Diseño Arquitectónico

DAGP | PLANEACIÓN Y DISEÑO DE PROYECTOS

PROYECTO CMV84-V01-Farmacia Hospitalaria Unidosis Etapa 2

CÓDIGO ARQ-01 Planta Arquitectónica

REVISIÓN 02 **FECHA** 22/05/2026

ESCALA 1 : 50 **DIBUJÓ** SDMG

UNIDAD DE SERVICIO Clínica Vidriera